



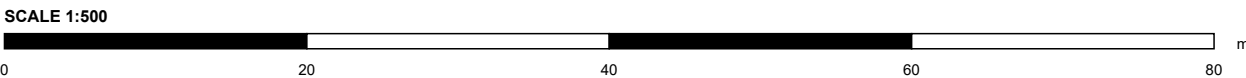

- LEGEND**
- I Precast wall panel joint, 3.0 m centres
 - III Louvre band — cooling air intake
 - Roof plant / PV array — hidden behind parapet
 - Aviation obstacle light
 - ▽ Level marker

- NOTES**
- Elevation is a diagrammatic composite of one typical Data Hall (identical for Halls 1-4), the Substation and the Admin/NOC block. True plan positions are on Site Plan PDC-DWG-001 — the three buildings do not sit on a common east-west sightline, so gaps shown are for clarity only.
 - Precast concrete wall panels, vertical joints at 3.0 m centres, typical all elevations.
 - Existing ground falls approximately 4 m from the north to the south site boundary; FFL is held level at +0.000 across all buildings — refer Civil drawings for cut/fill and retaining details.
 - Roof-mounted plant and the PV array are set back from the roof edge and screened from view by the parapet upstand.
 - Aviation obstacle lighting to the highest point on site (data hall parapet, +9.500) per Traficom requirements.
 - Louvre bands are cooling-system fresh-air intakes; final sizing and count by the Mechanical sub-contractor.

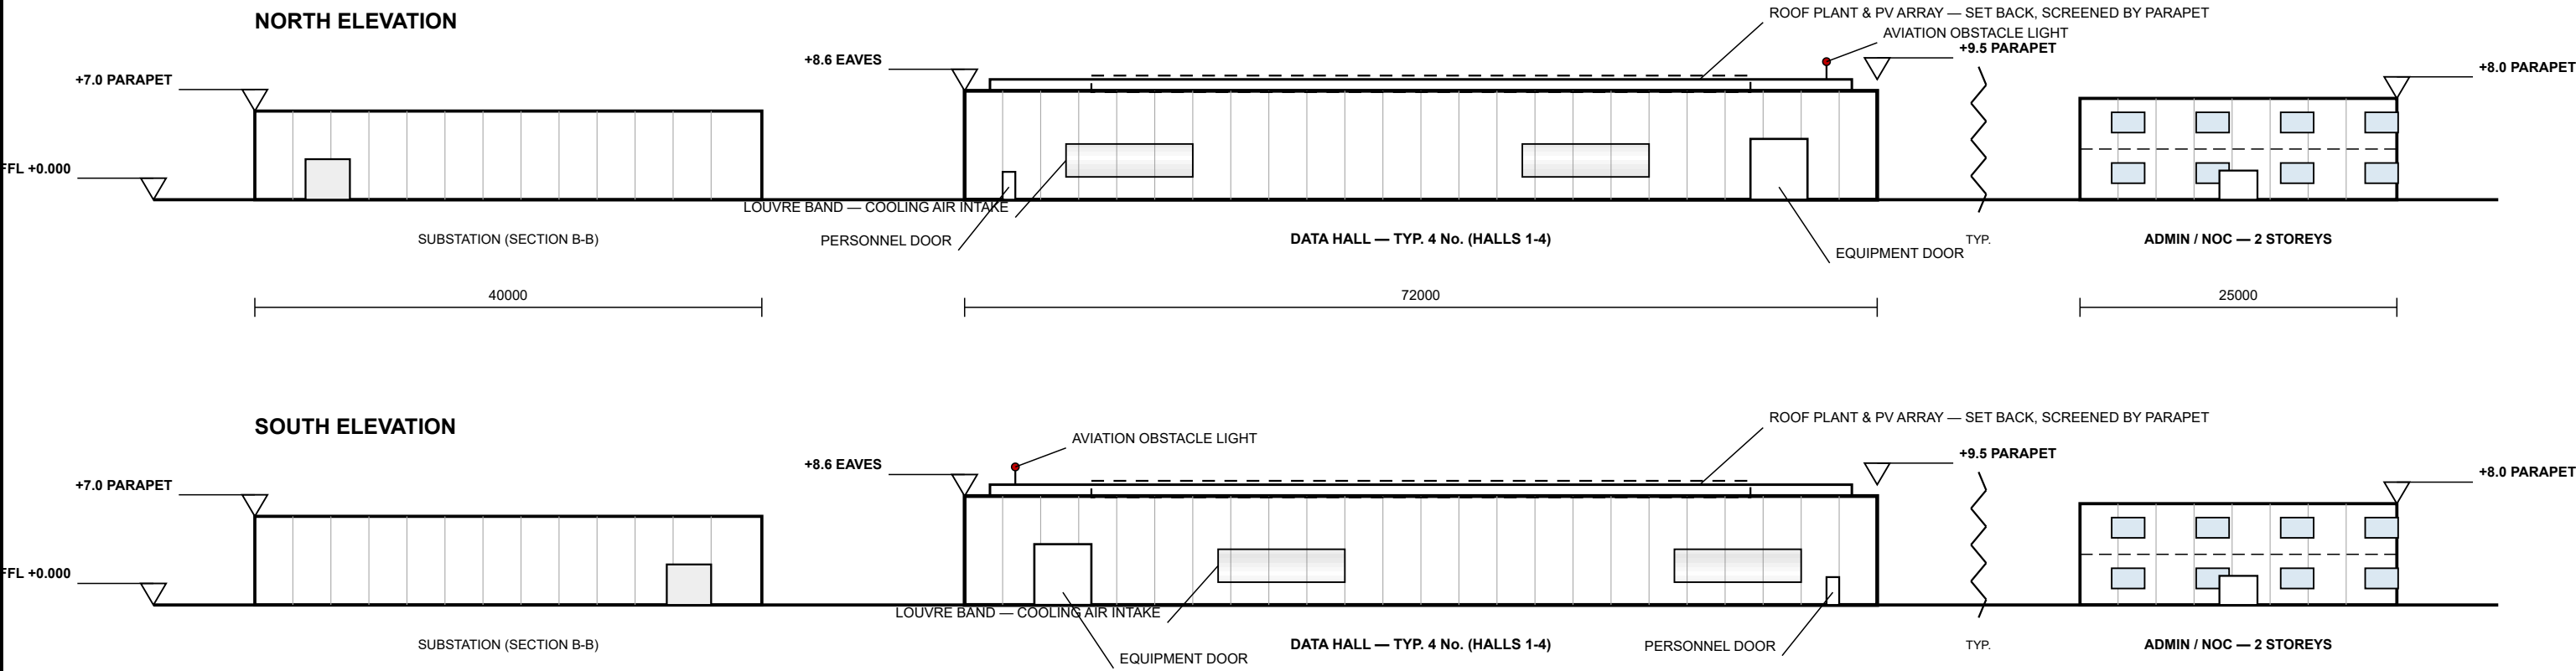

PROJECT POLARIS DC-1 — AVIAPOLIS DATA CAMPUS, PHASE...			
EMPLOYER POLARIS DIGITAL INFRASTRUCTURE OY			
CONTRACTOR NORDBUILD OY			
DRAWING ELEVATIONS — NORTH & SOUTH			
DISCIPLINE ARCHITECTURAL			
DWG No PDC-DWG-006 SYNTHETIC DEMONSTRATION DATA — NOT A REAL PROJECT	REV A	DATE 24.02.2026	SCALE 1:500