



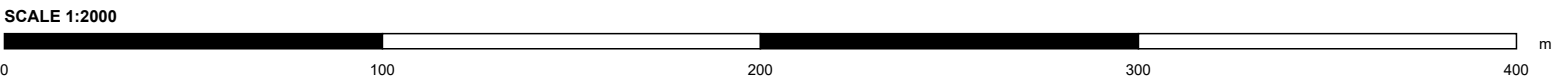

- LEGEND**
- Plot boundary — the contract site
 - Existing buildings (neighbour, not this contract)
 - Public highway
 - Shared private access road
 - Site access gate — the only one
 - Retained tree belt — 5 m no-encroachment

- NOTES**
- Base plan for the site logistics plan required by PDC-LOG-001. Shows the plot and the ground around it — approach roads, the site access junction and the neighbouring operator.
 - SITE ACCESS FROM TIKKURILANTIE ONLY.** The access road is shared with an operating logistics neighbour whose vehicles use it throughout. Deliveries 06:00-22:00 weekdays (PDC-CAL-001).
 - There is ONE gate. No second point of entry exists and none is permitted without the planning authority's consent.
 - Tikkurilantie is a single carriageway each way with a 50 km/h limit. No queuing on the highway at any time — vehicles wait inside the gate or not at all.
 - The 110 kV overhead line crosses the north-east of the plot. Crane operation within its exclusion zone requires the network operator's written permission (PDC-DWG-001).
 - Tree belt to the north and east is subject to a retention condition — no storage, plant or spoil within 5 m of the trunks.
 - Levels fall approximately 1.5 m from east to west across the plot. Surface water runs to the western ditch.

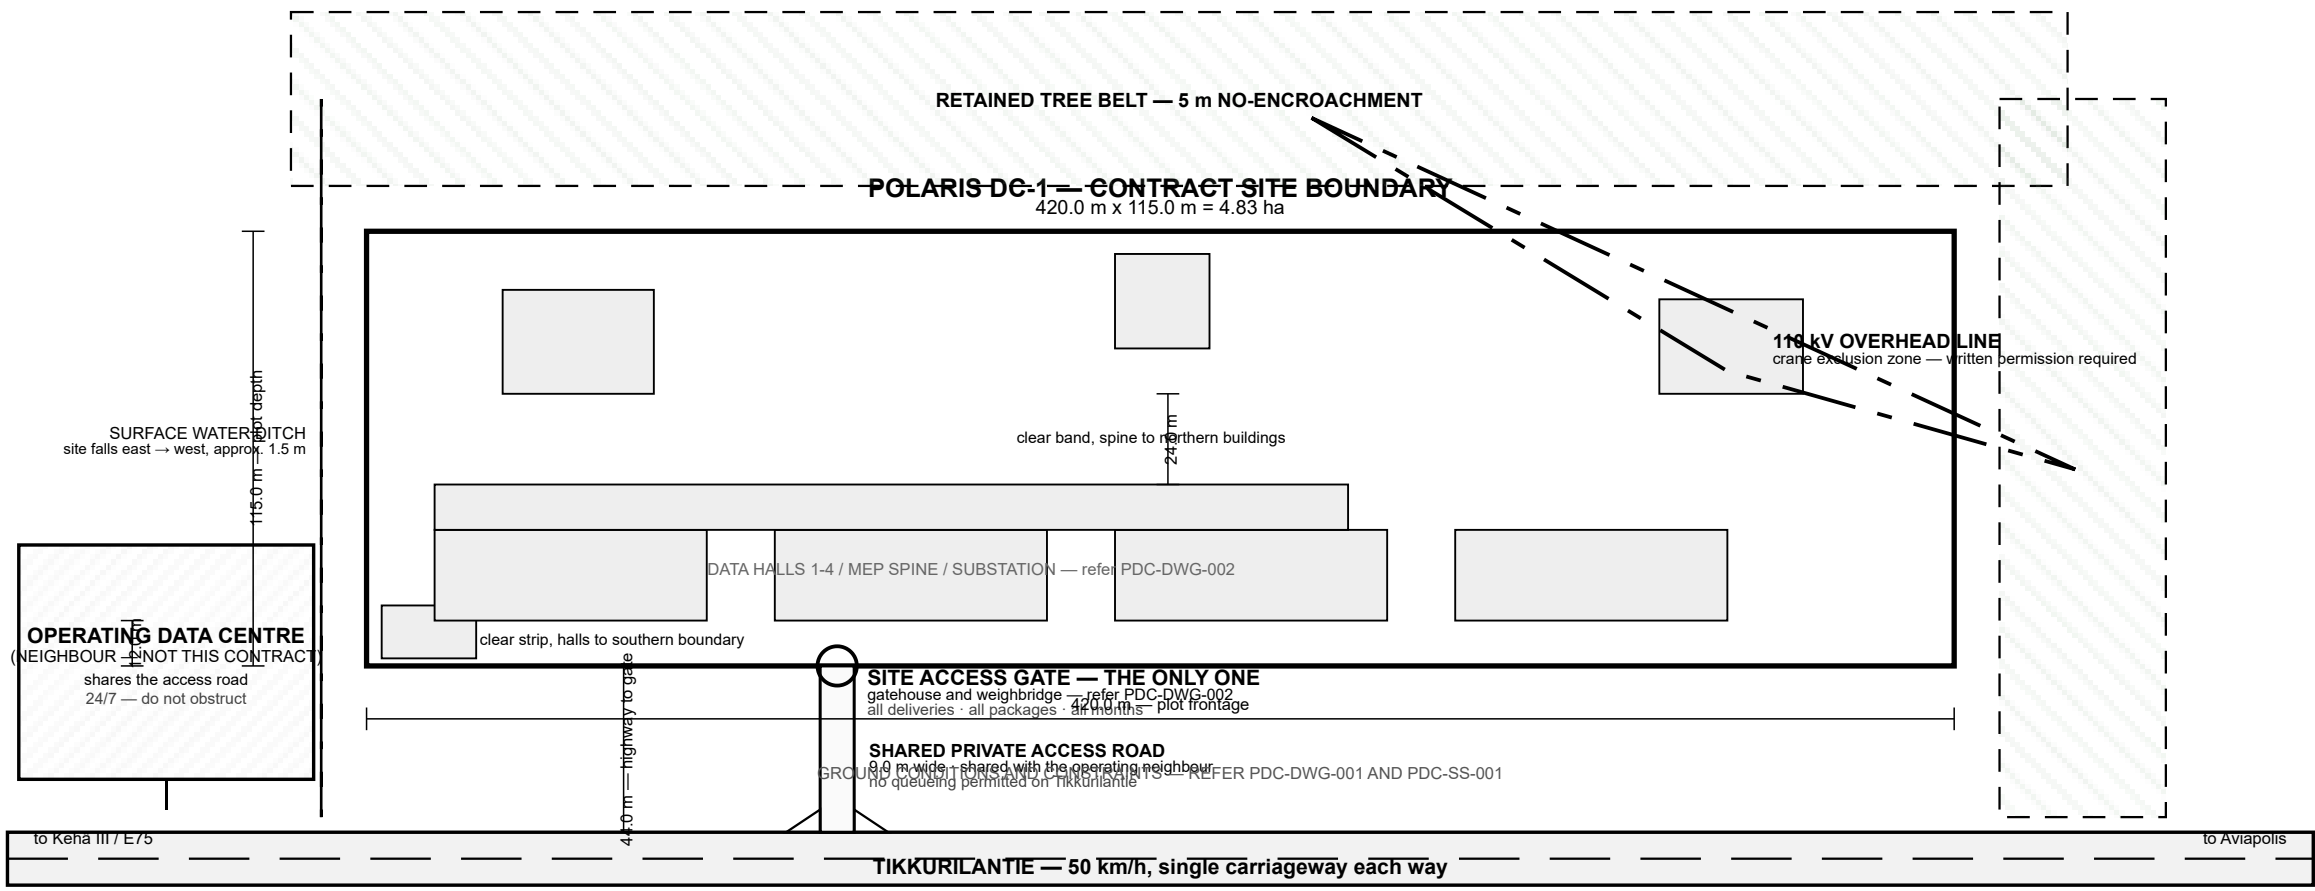

PROJECT
POLARIS DC-1 — AVIAPOLIS DATA CAMPUS, PHASE...

EMPLOYER
POLARIS DIGITAL INFRASTRUCTURE OY

CONTRACTOR
NORDBUILD OY

DRAWING
SITE LOGISTICS BASE PLAN

DISCIPLINE
LOGISTICS

DWG No
PDC-DWG-017

SYNTHETIC DEMONSTRATION DATA — NOT A REAL PROJECT

REV
A

DATE
24.02.2026

SCALE
1:2000